

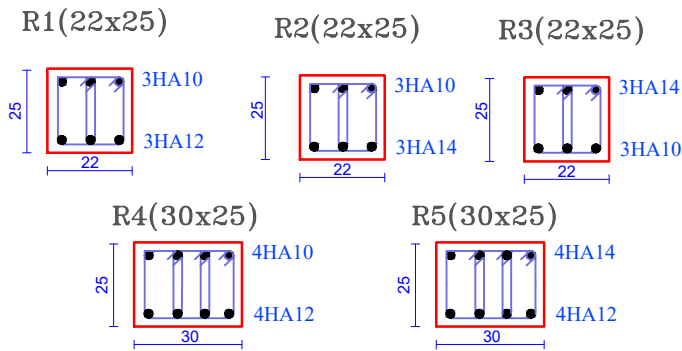


DÉTAILS RAIDISSEURS

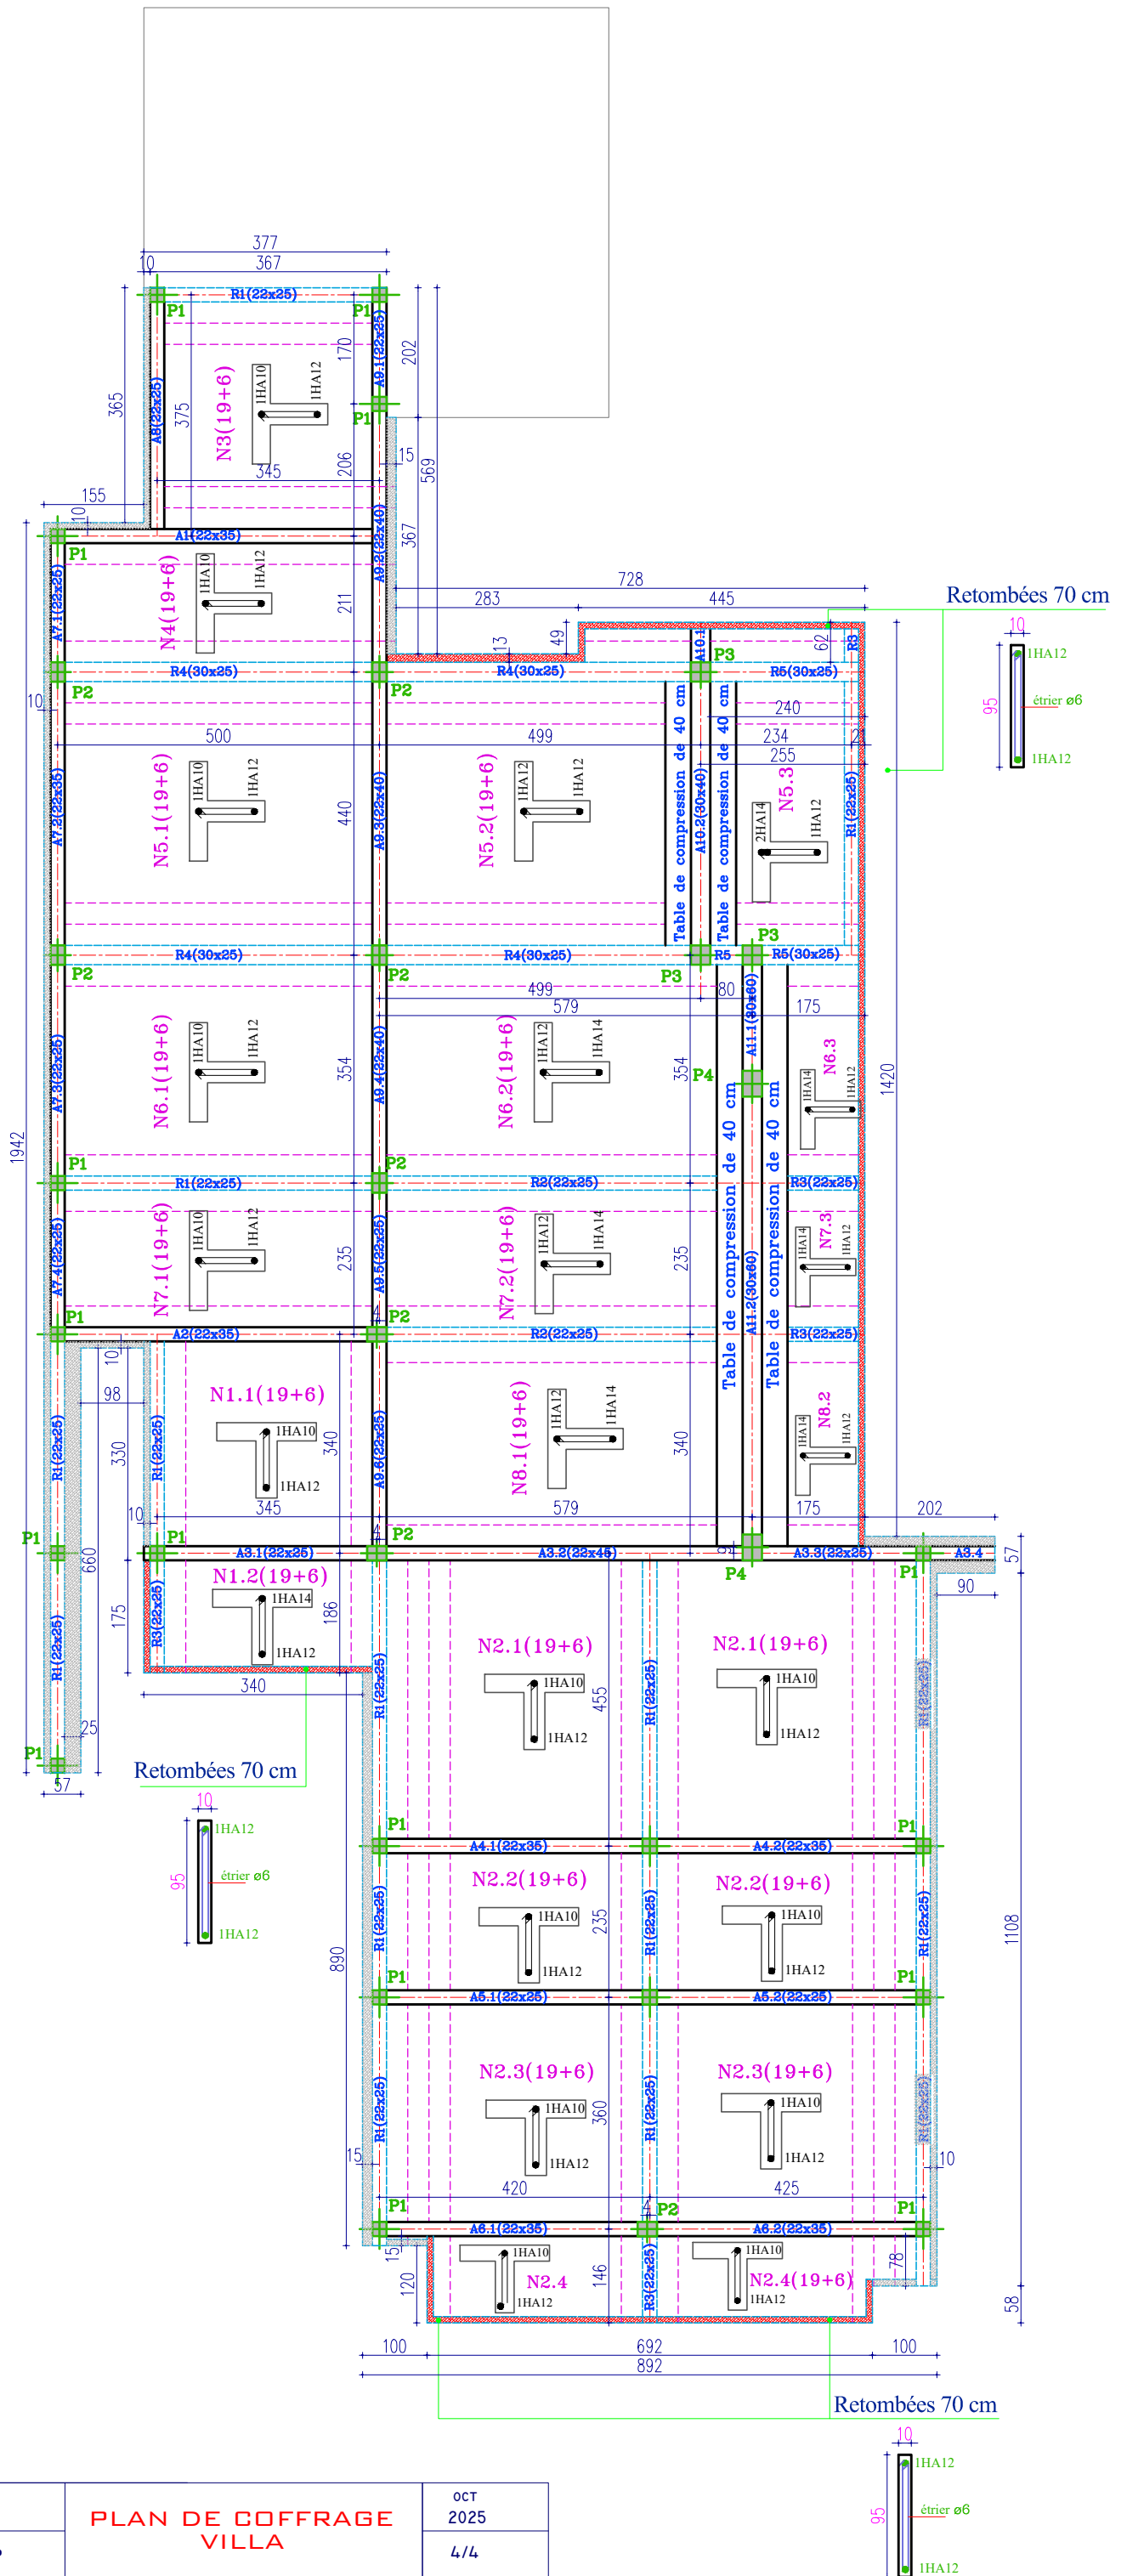

DETAILS DES POTEaux

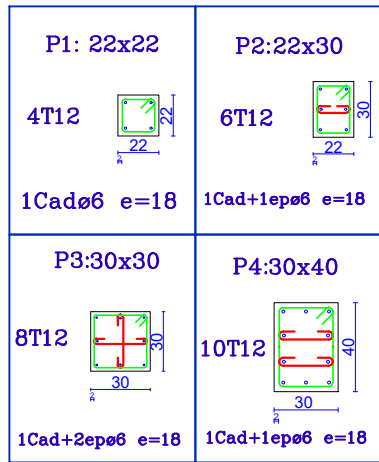

ING STRUCTURE : Mohamed Adnene Karkri
TEL: 20 359 424
ADRESSE: AVENUE REPUBLIQUE,
BENI KHALLED 8021- NABEUL
FB: JK BUILDING
EMAIL: MED.ADNENE.KARKRI@GMAIL.COM

PROJET DE
CONSTRUCTION D'UNE
VILLA
PROPRIETAIRE : FAMILLE HMAIED

PLAN DE COFFRAGE
VILLA

OCT
2025
4/4