



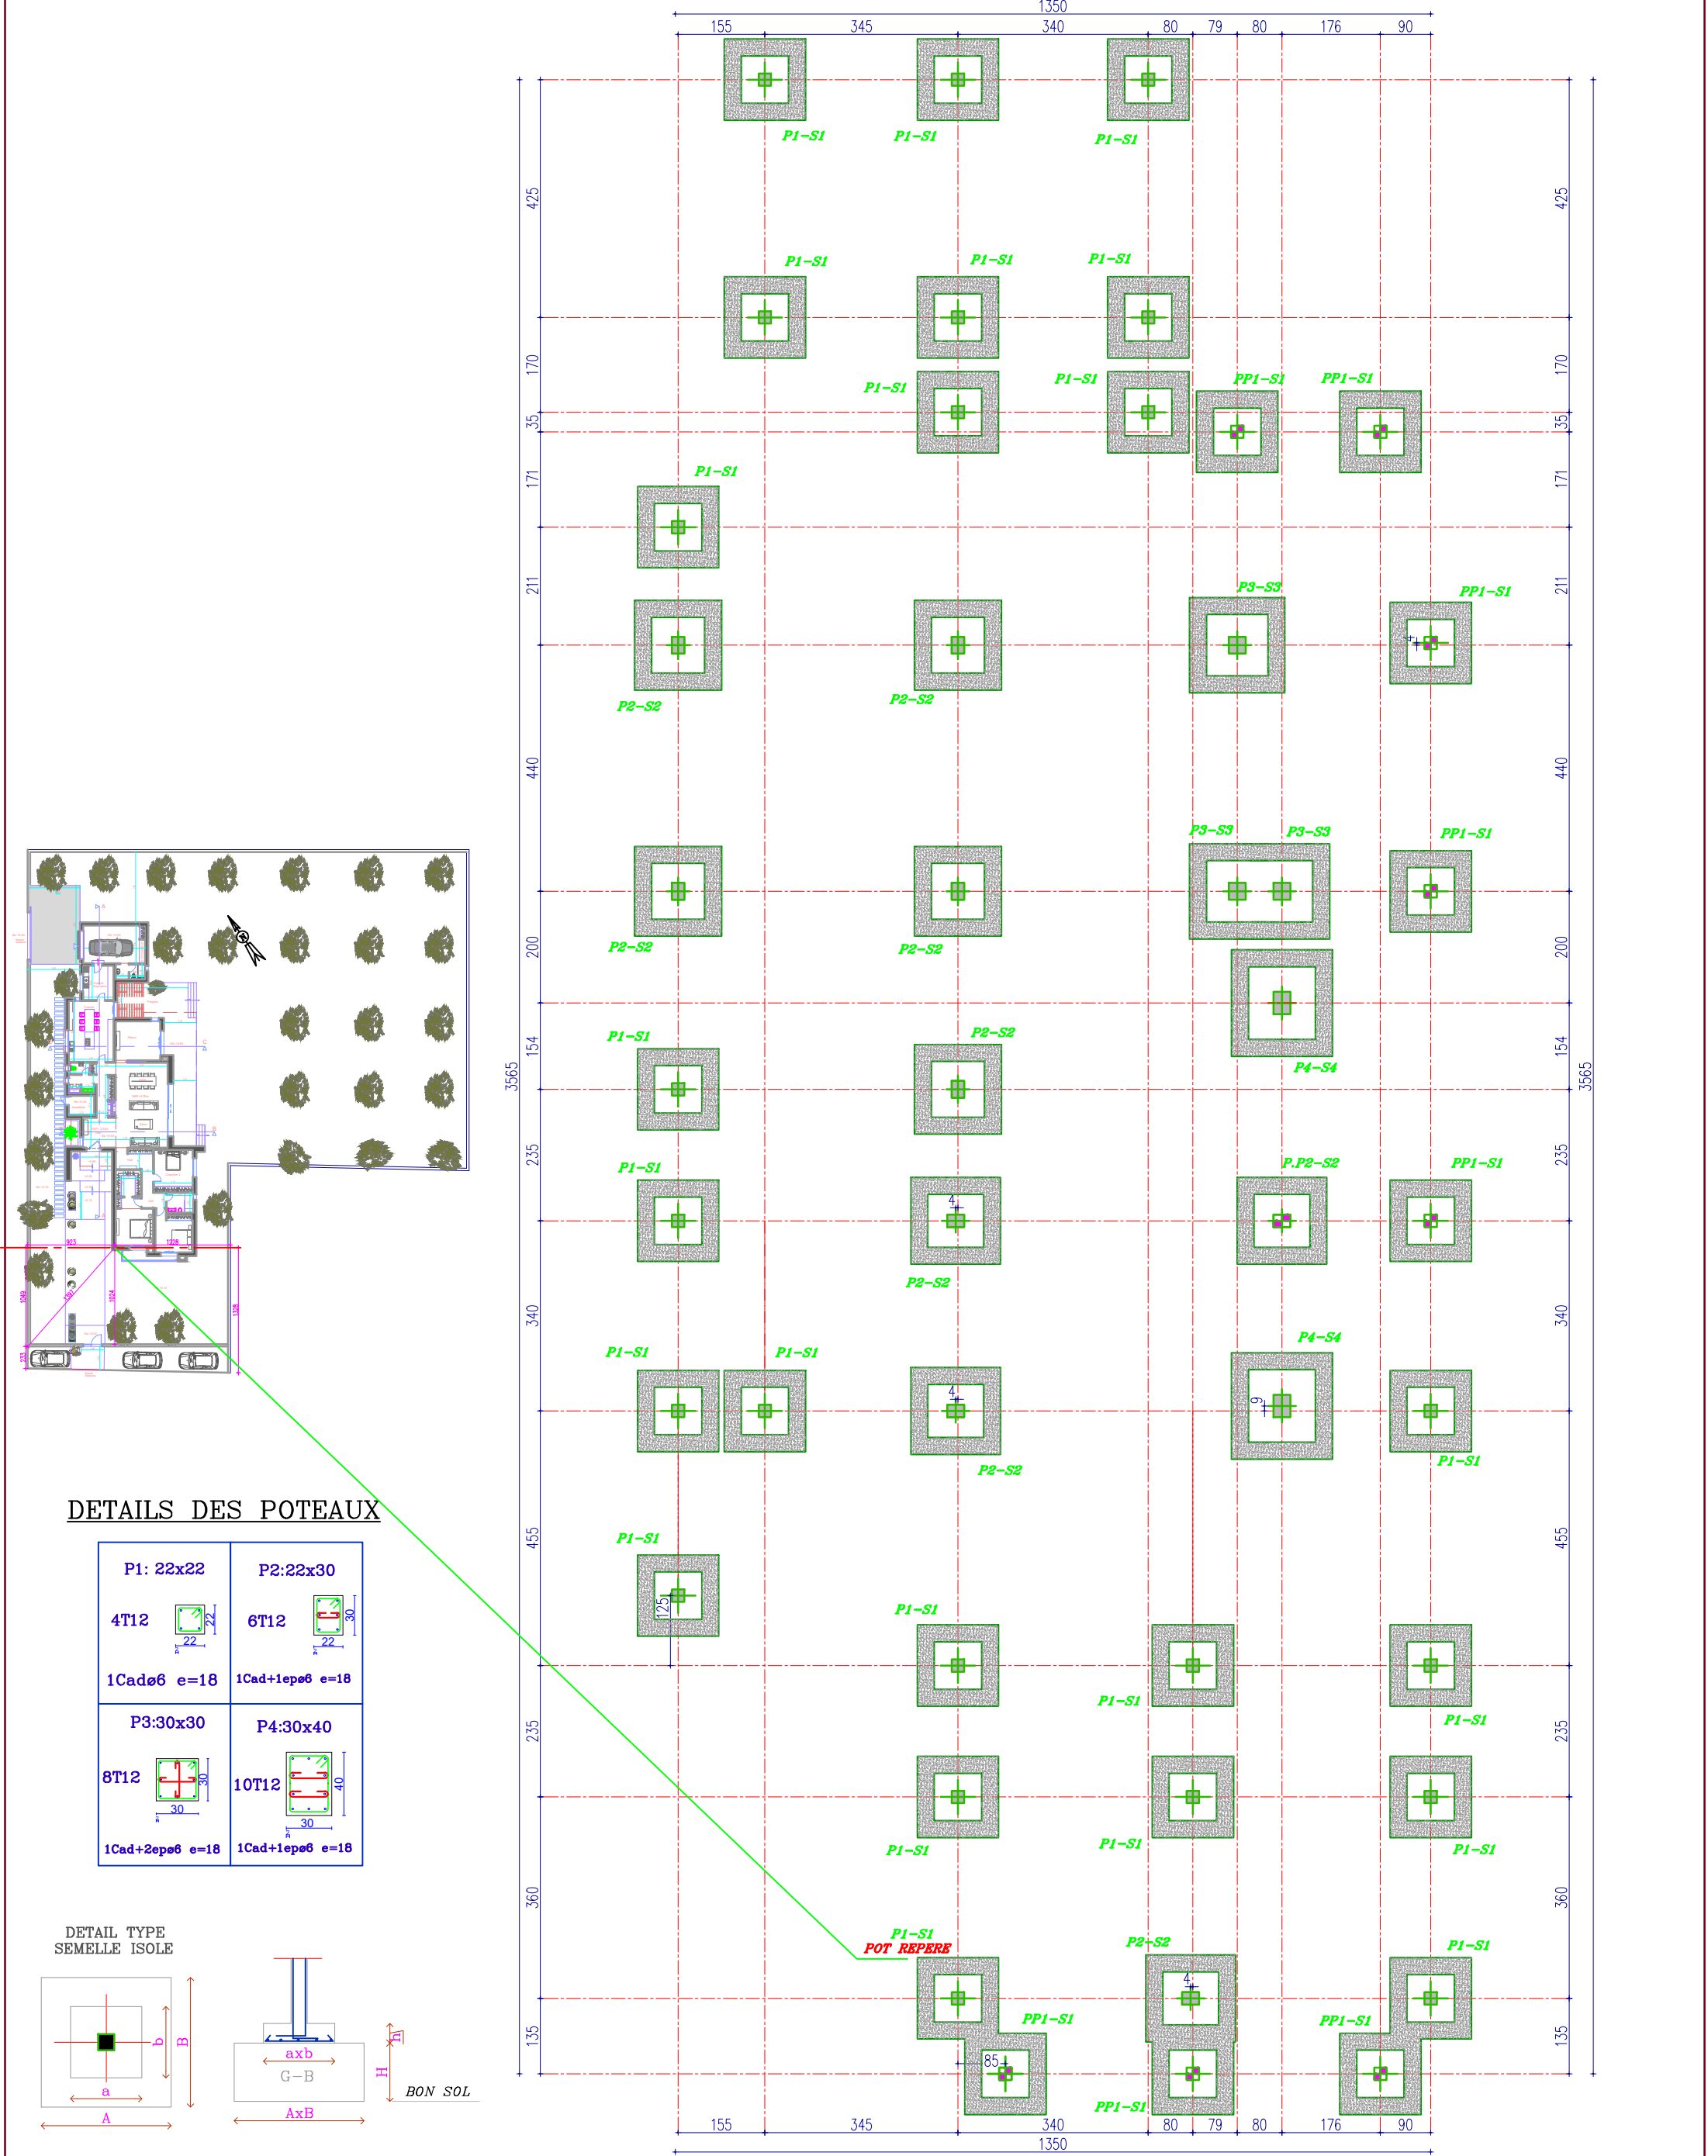

DETAILS DES POTEAUX

P1: 22x22 4T12 1Cadø6 e=18	P2:22x30 6T12 1Cad+1epø6 e=18
P3:30x30 8T12 1Cad+2epø6 e=18	P4:30x40 10T12 1Cad+1epø6 e=18

DETAIL TYPE
SEMELLE ISOLE

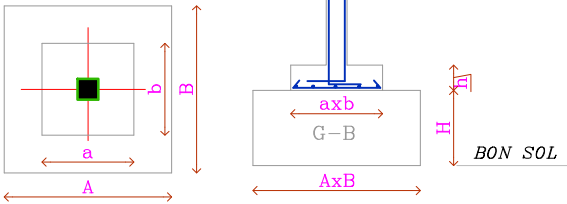

Section	Semelle	Gros béton AxBxH			Ferrailage semelle	
	axbxb	1.5 bar	2 bar	2.5 bar		
P1: 22x22	85x85x25	170x170x85	145x145x60	130x130x45	#6T12	#6T12
P2: 22x30	95x100x30	190x195x95	165x170x70	145x150x50	#7T12	#8T12
P3: 30x30	110x110x35	220x220x110	190x190x80	170x170x60	#9T12	#9T12
P3: 30x40	120x130x35	240x250x120	210x220x90	185x195x65	#10T14	#11T14