



R1(22x25)

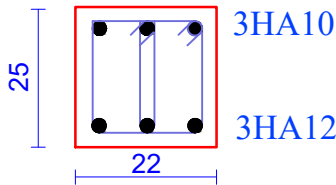

DETAILS DES POTEAUX

P1: 22x22 4T12 1Cadø6 e=18	P2: 22x30 6T12 1Cad+1epø6 e=18
P3: 30x30 8T12 1Cad+2epø6 e=18	P4: 30x40 10T12 1Cad+1epø6 e=18

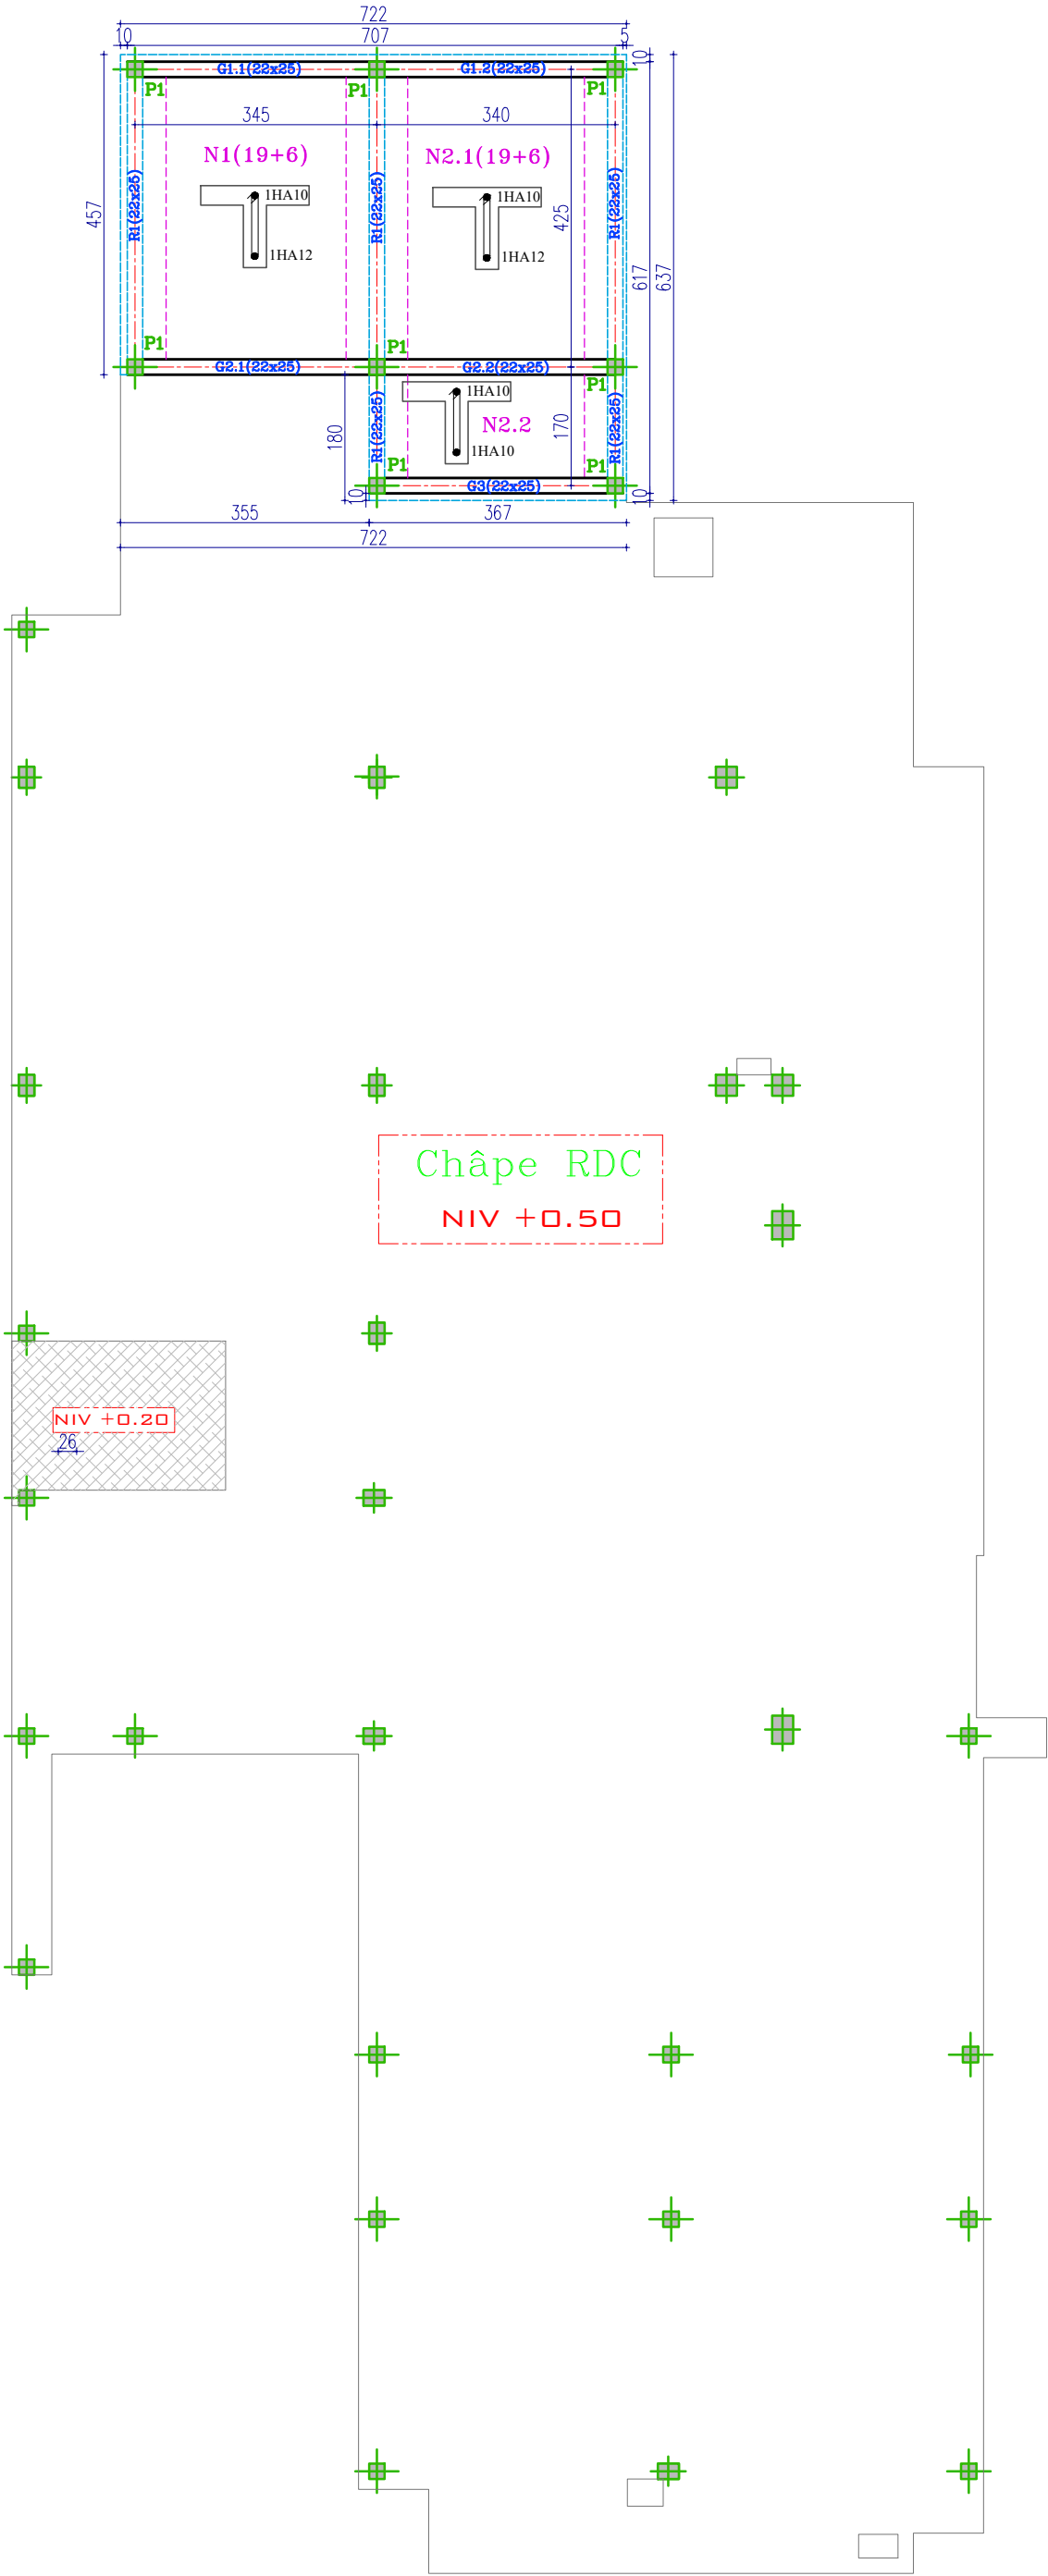

ING STRUCTURE : Mohamed Adnene Karkri
TEL: 20 359 424
ADRESSE: AVENUE REPUBLIQUE,
BENI KHALLED 8021- NABEUL
FB: JK BUILDING
EMAIL: MED.ADNENE.KARKRI@GMAIL.COM

PROJET DE
CONSTRUCTION D'UNE
VILLA
PROPRIETAIRE : FAMILLE HMAIED

PLAN DE COFFRAGE
GARAGE

OCT
2025
3/4